


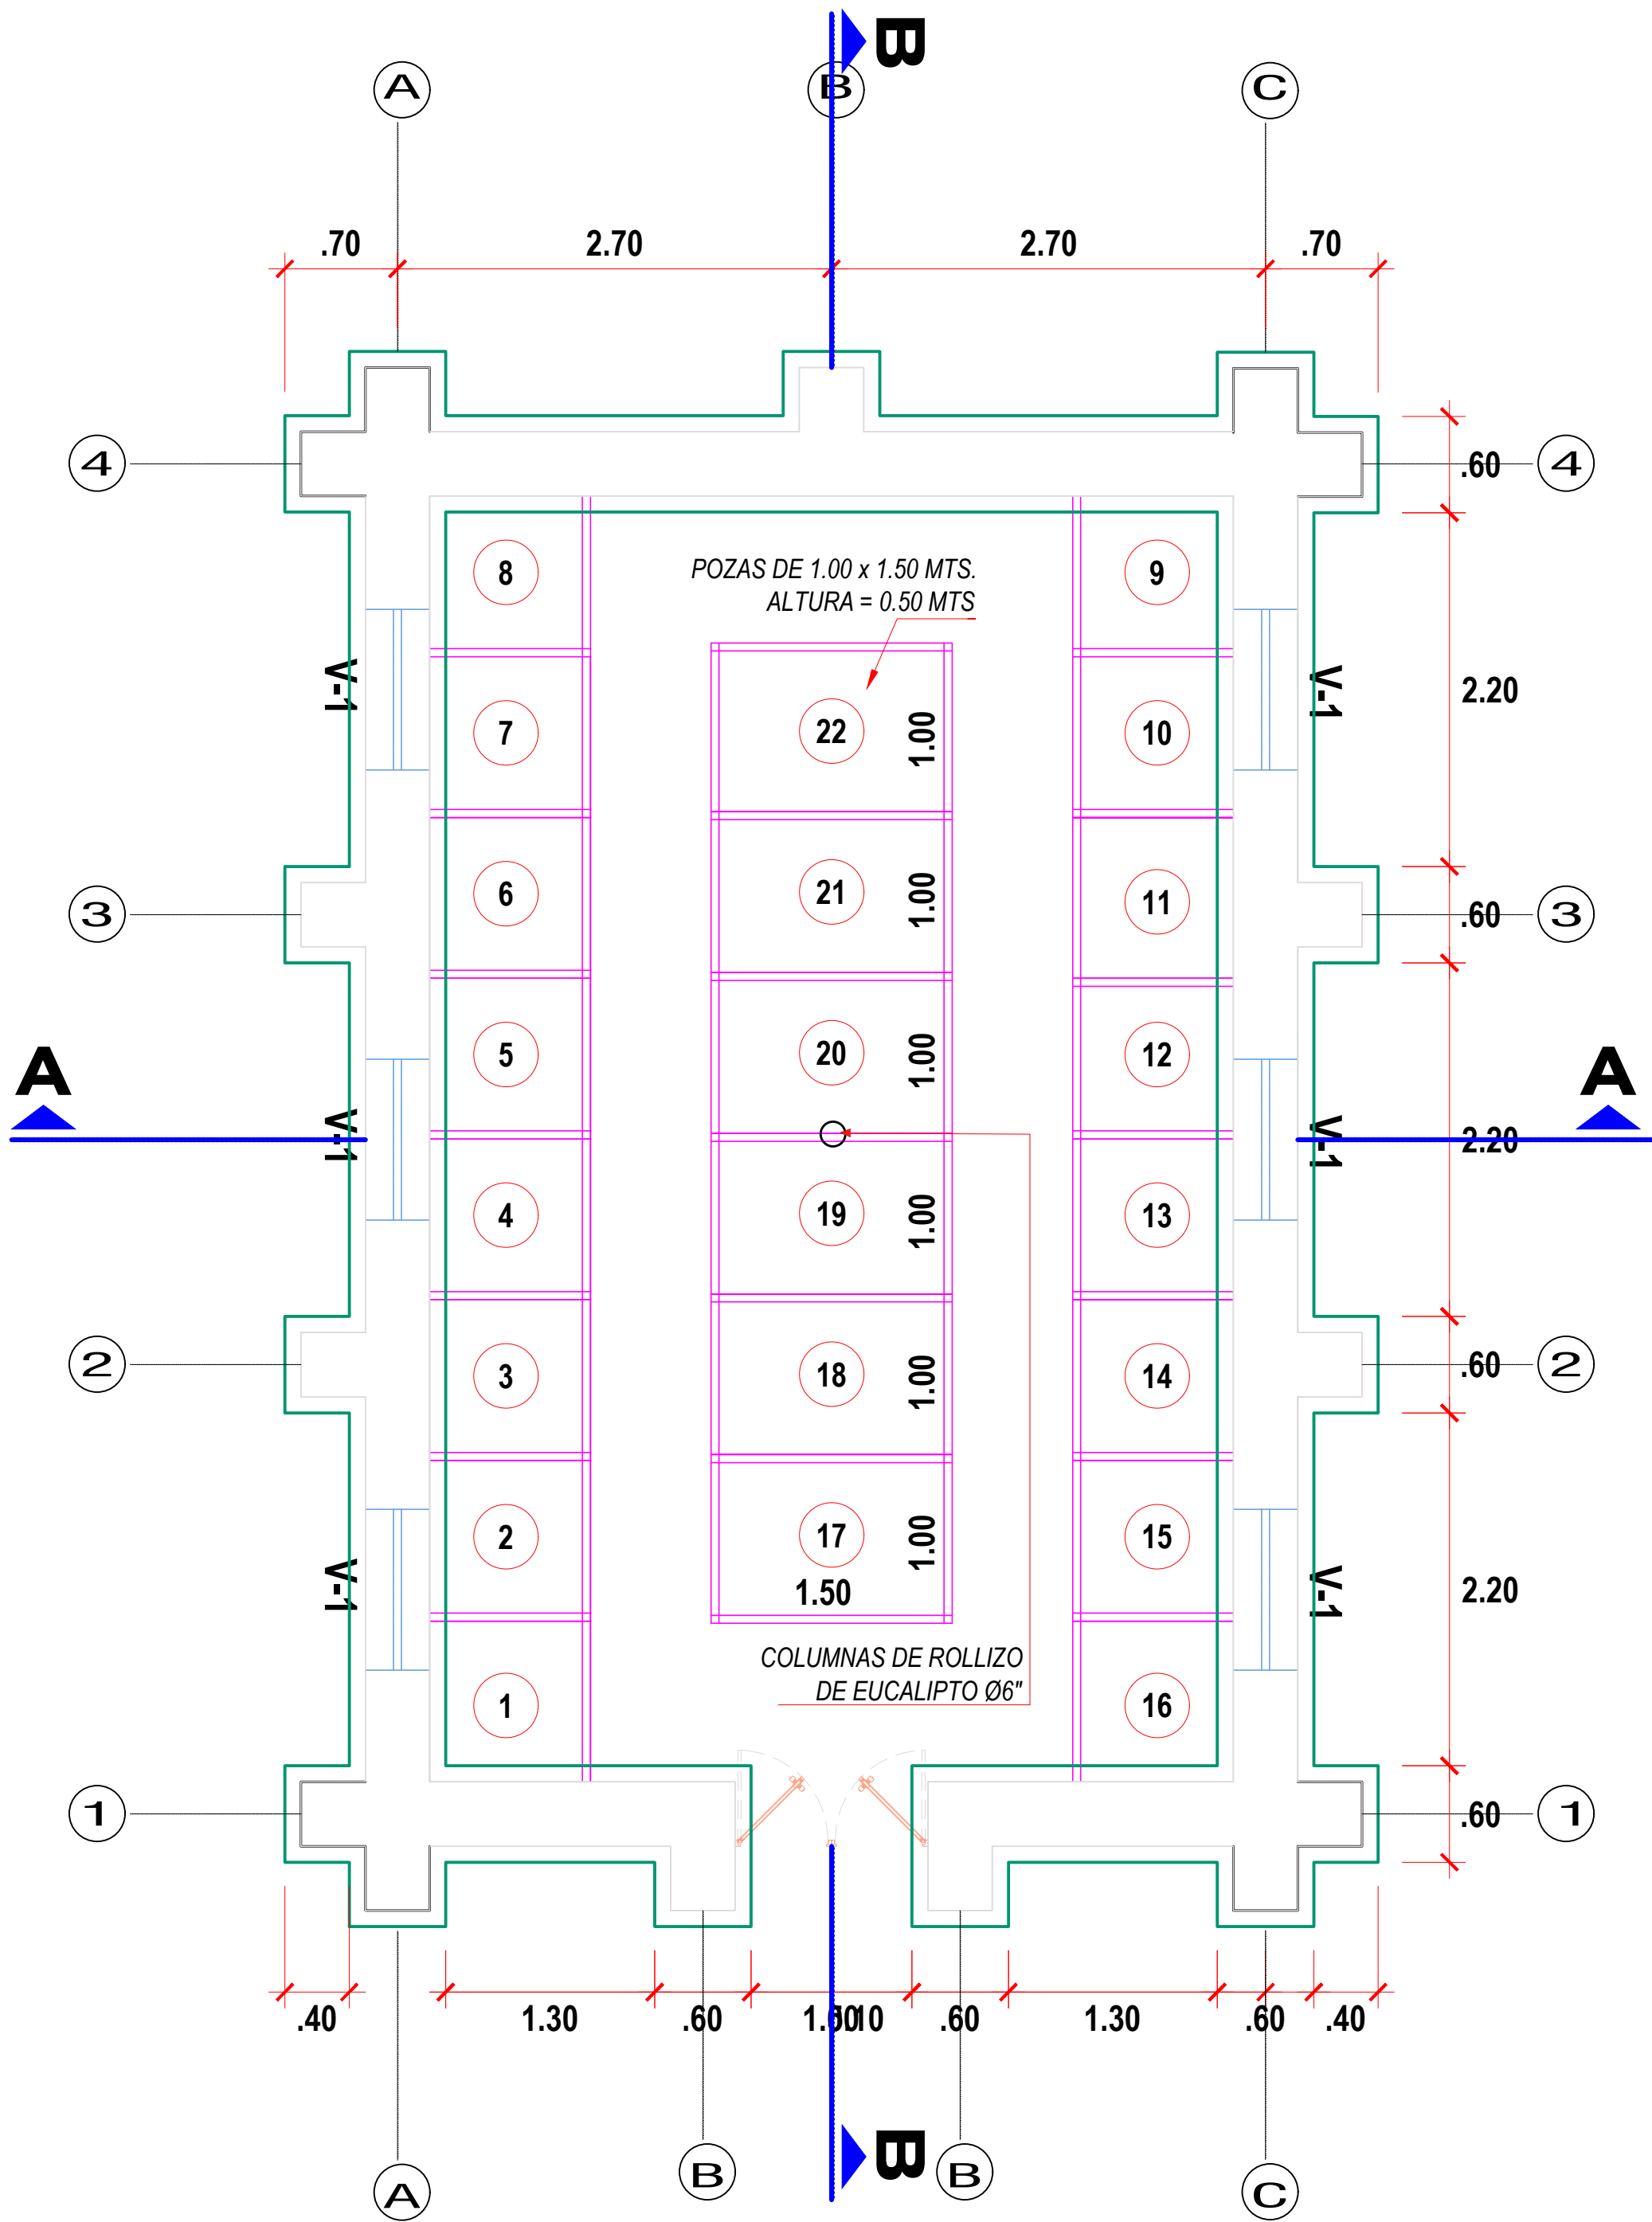

PLANO DE CIMENTACION

ESCALA : 1/50



ESPECIFICACIONES TECNICAS

CONCRETO :

CIMIENTO MEZCLA BARRO + PM (6" máx)
SOBRECIMIENTO MEZCLA BARRO + PG (8" máx)

MUROS:

MURO DE ADOBE ASENTADO CON BARRO, 0.40"x0.25"x0.18

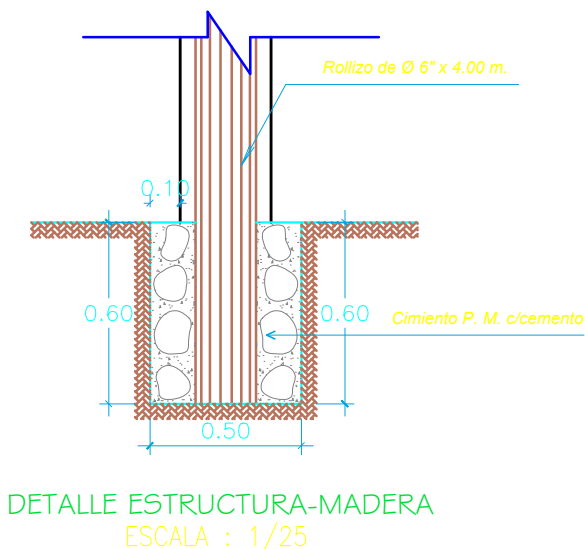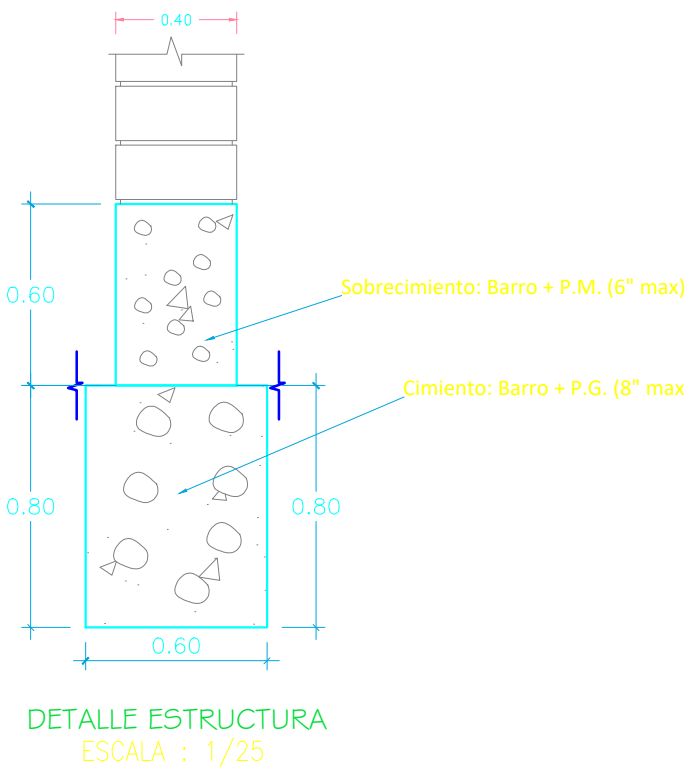

"ASOCIACION DE PRODUCTORES AGROPECUARIOS LAMBRASHUAYCCO DE CASAORCCO (APAL)"				
PROYECTO: "MEJORAMIENTO EN LA PRODUCCIÓN Y COMERCIALIZACIÓN DE CUYES" DE LA ASOCIACIÓN DE PRODUCTORES AGROPECUARIOS LAMBRASHUAYCCO DE CASAORCCO (APAL) DEL DISTRITO DE CARMEN ALTO, PROVINCIA HUAMANGA - AYACUCHO"			LAMINA: E- 01	
PLANO: PLANO DE CIMENTACION				
UBICACIÓN : Departamento : AYACUCHO Provincia : HUAMANGA Distrito : CARMEN ALTO Sector : CASAORCCO		DIBUJO: R.B.H. FECHA: AGOSTO 2020	DISEÑO: Ing. K.B.H. ESCALA: INDICADA	PROYECTISTA: Ing. K.B.H. V"B":
		APROBACION:		