



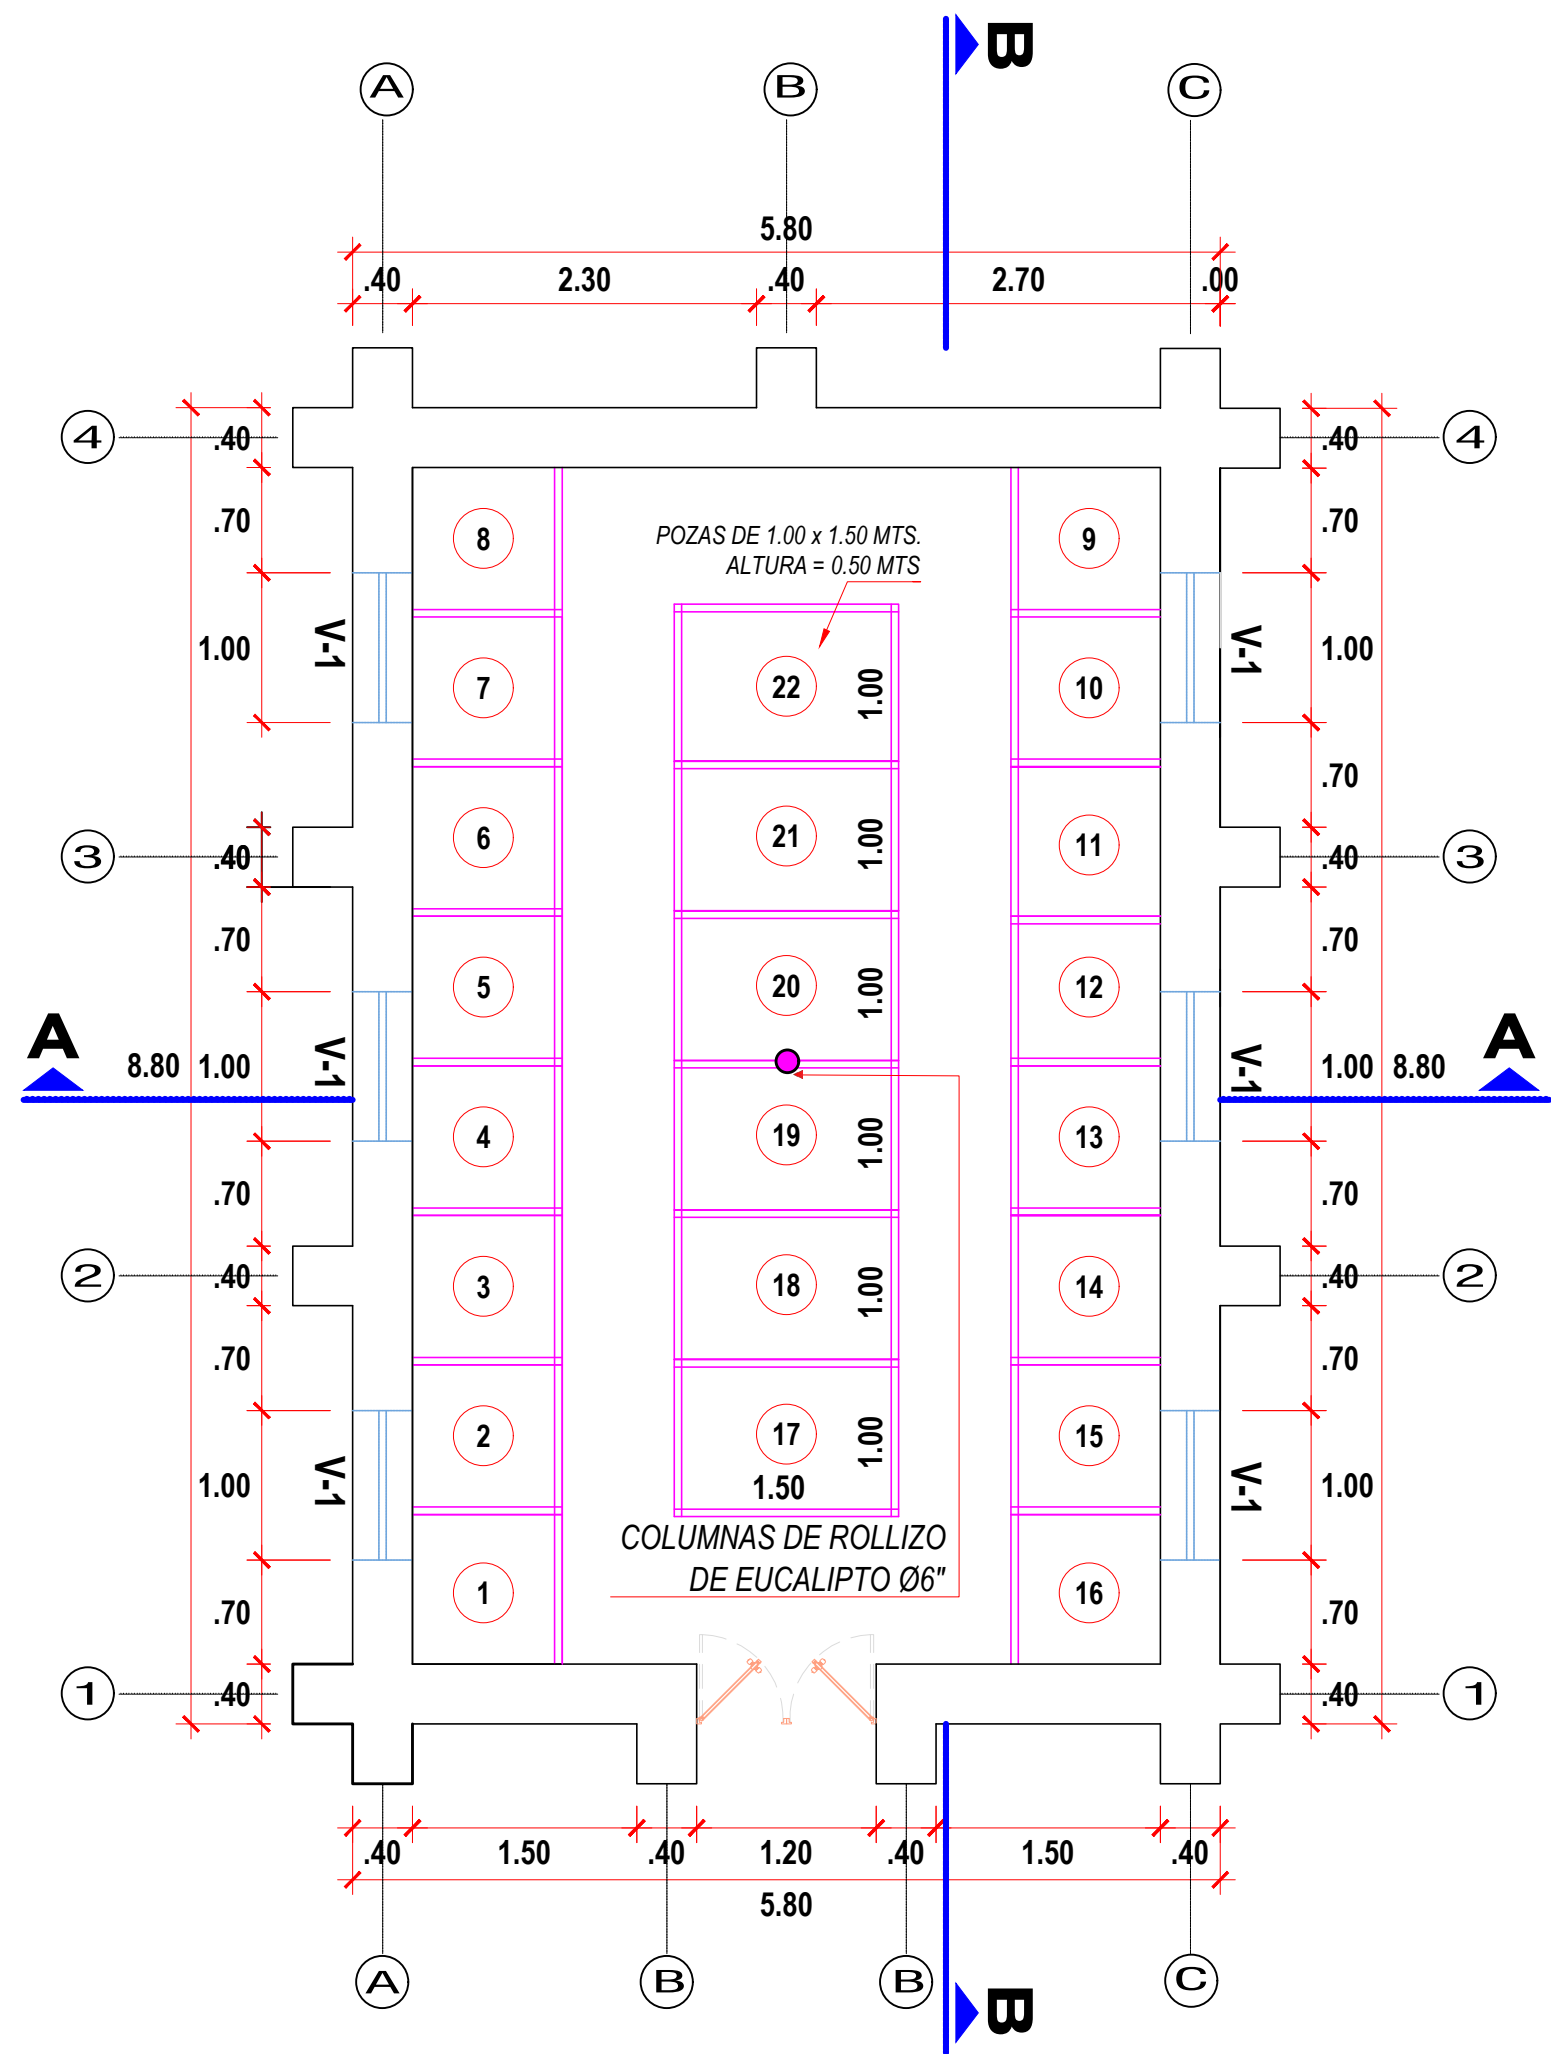


DISTRIBUCION


ESCALA : 1/50

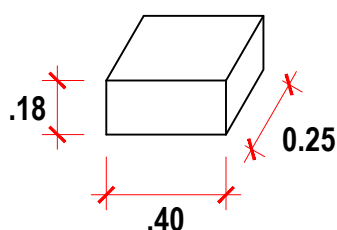


ADOBE TIPICO

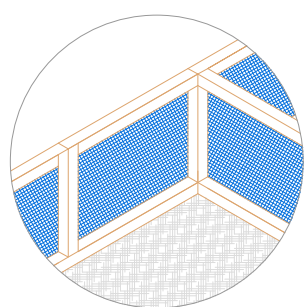

ISOMETRICO DE POSA DE CUY DE MALLA METALICO CON MARCO DE MADERA

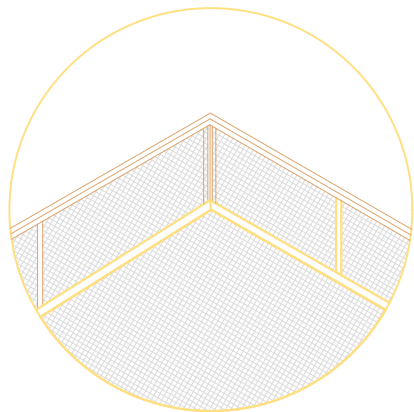


UNIONES PERSPECTIVA

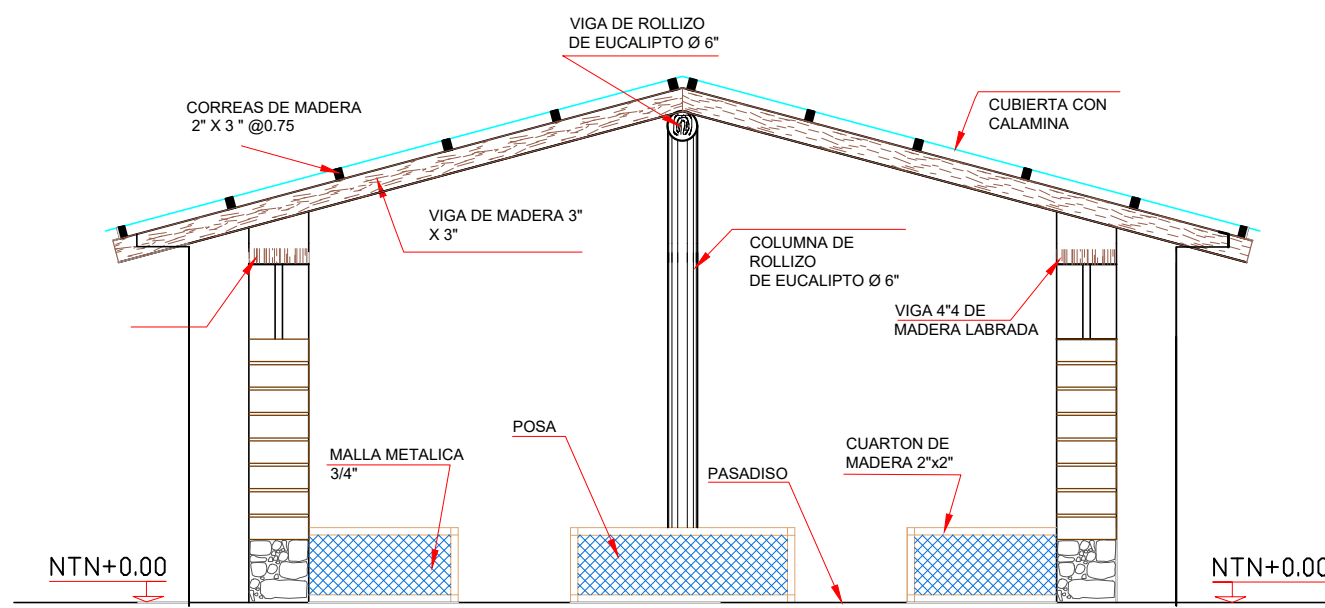

CORTE A-A


ESCALA : 1/50

CUADRO DE VANDOS						
TIPO	ANCHO	ALTO	ALFEIZAR	ESTRUCTURA	NOMBRE	CANT.
V1	1.00	0.50	1.76	MARCO DE MADERA CON MALLA MOSQUETERO	VENTANA TIPO V1	6
P1	1.20	2.00	-	MARCO DE MADERA DE 2 HOJAS CON CALAMINA	PUERTA TIPO P1	1

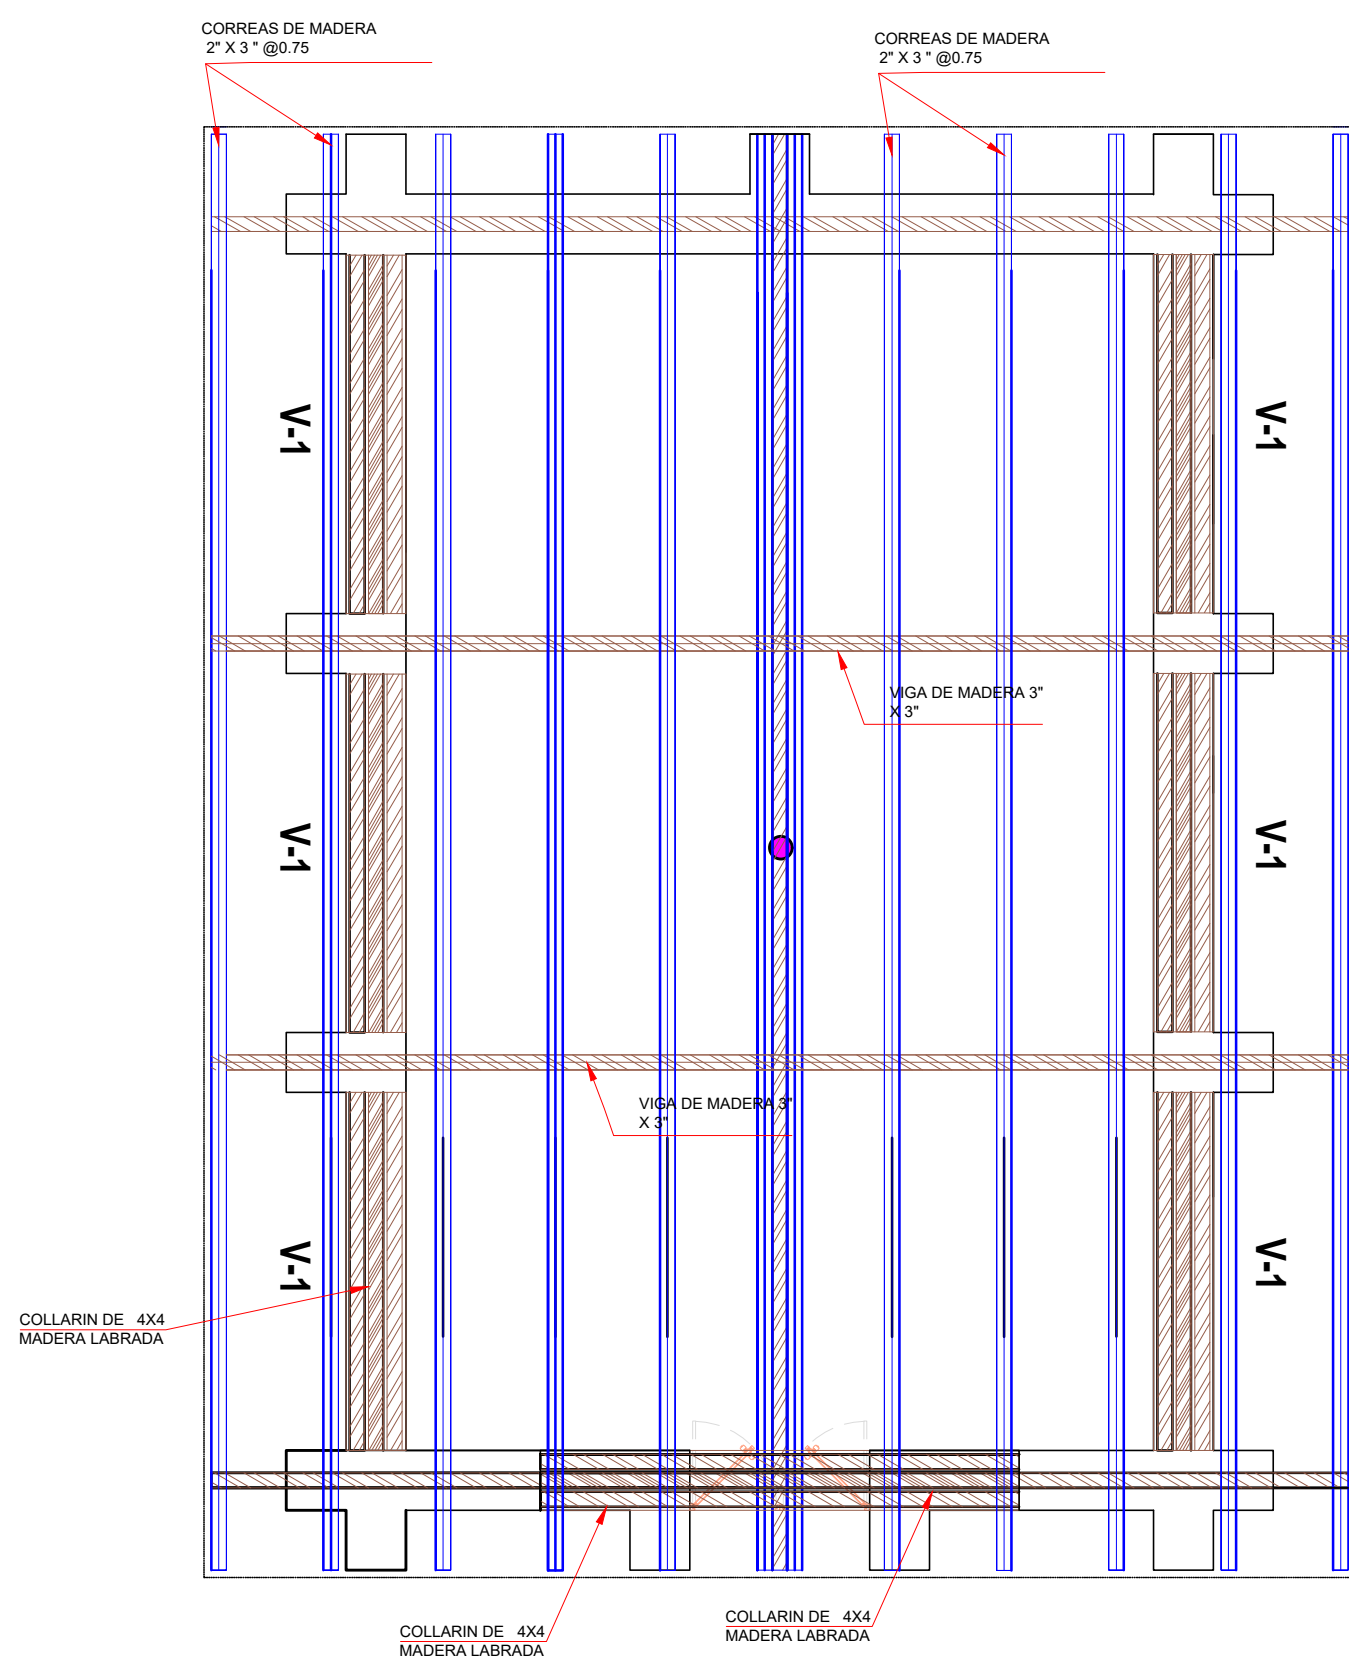


ESTRUCTURA DE TECHO

ESCALA : 1/50

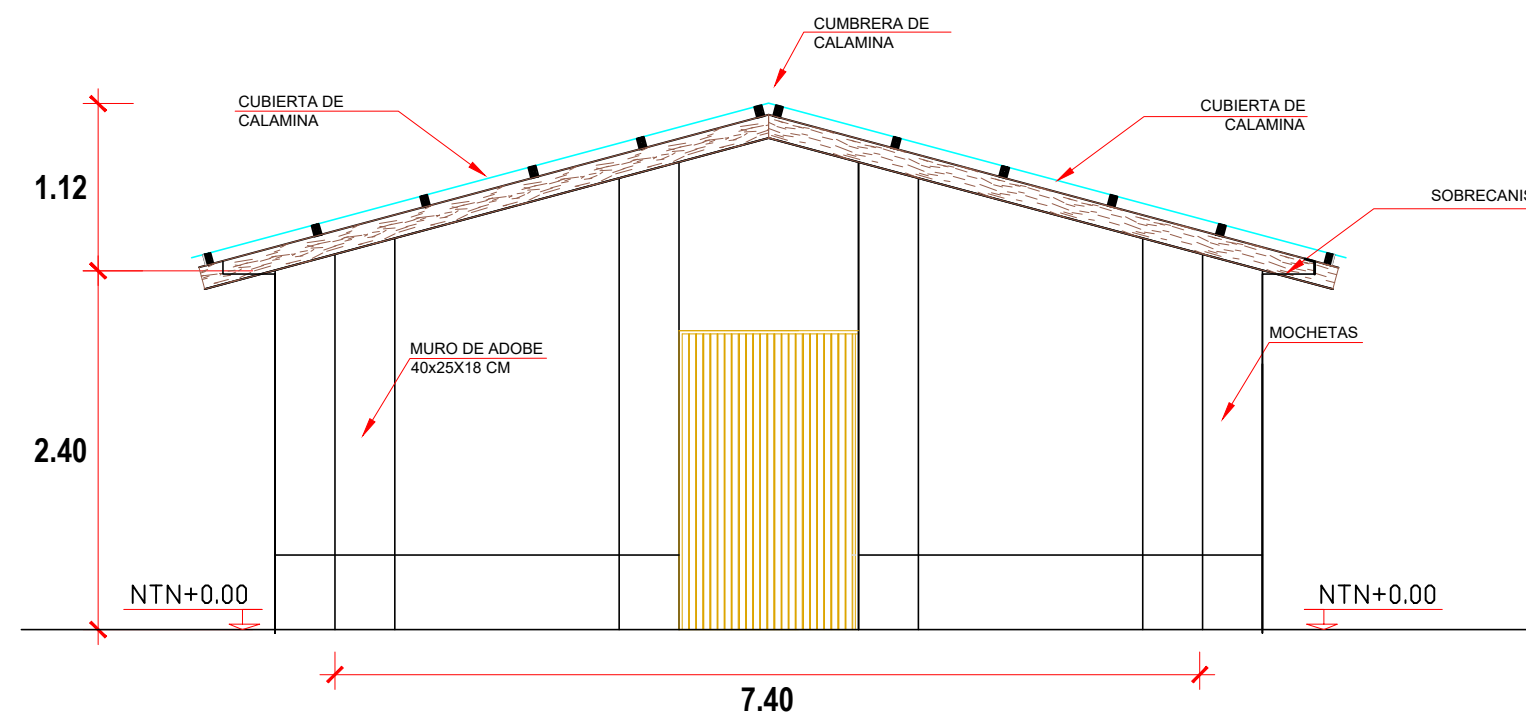


ELEVACION FRONTAL

ESCALA : 1/50

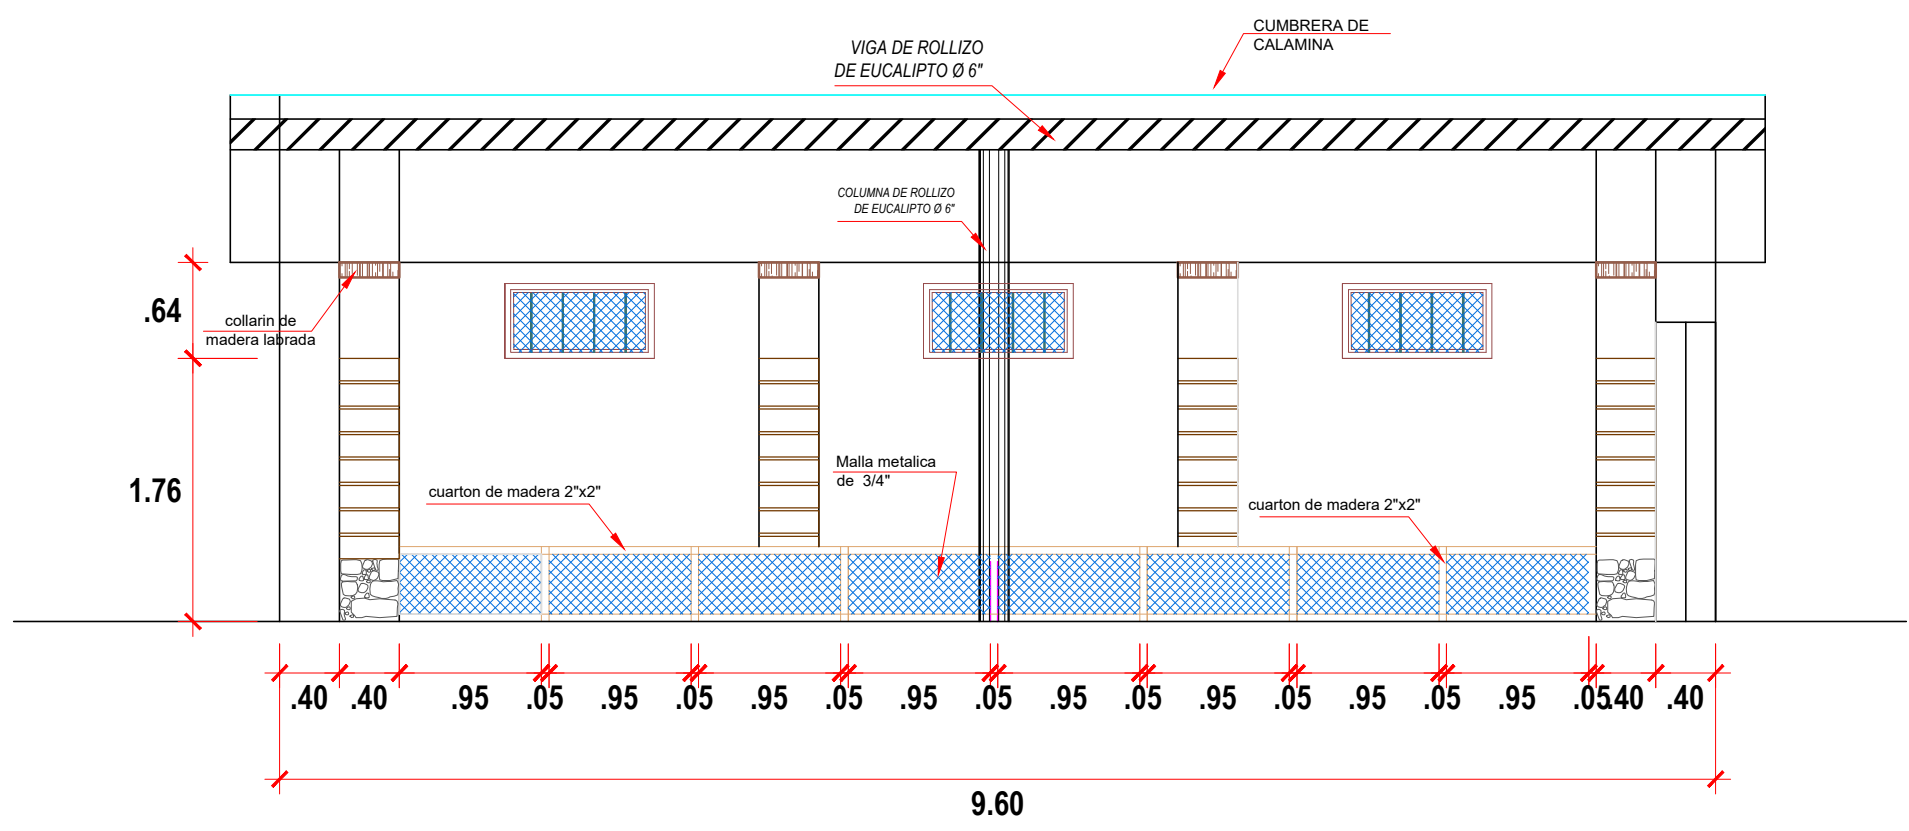

CORTE B-B

ESCALA : 1/50

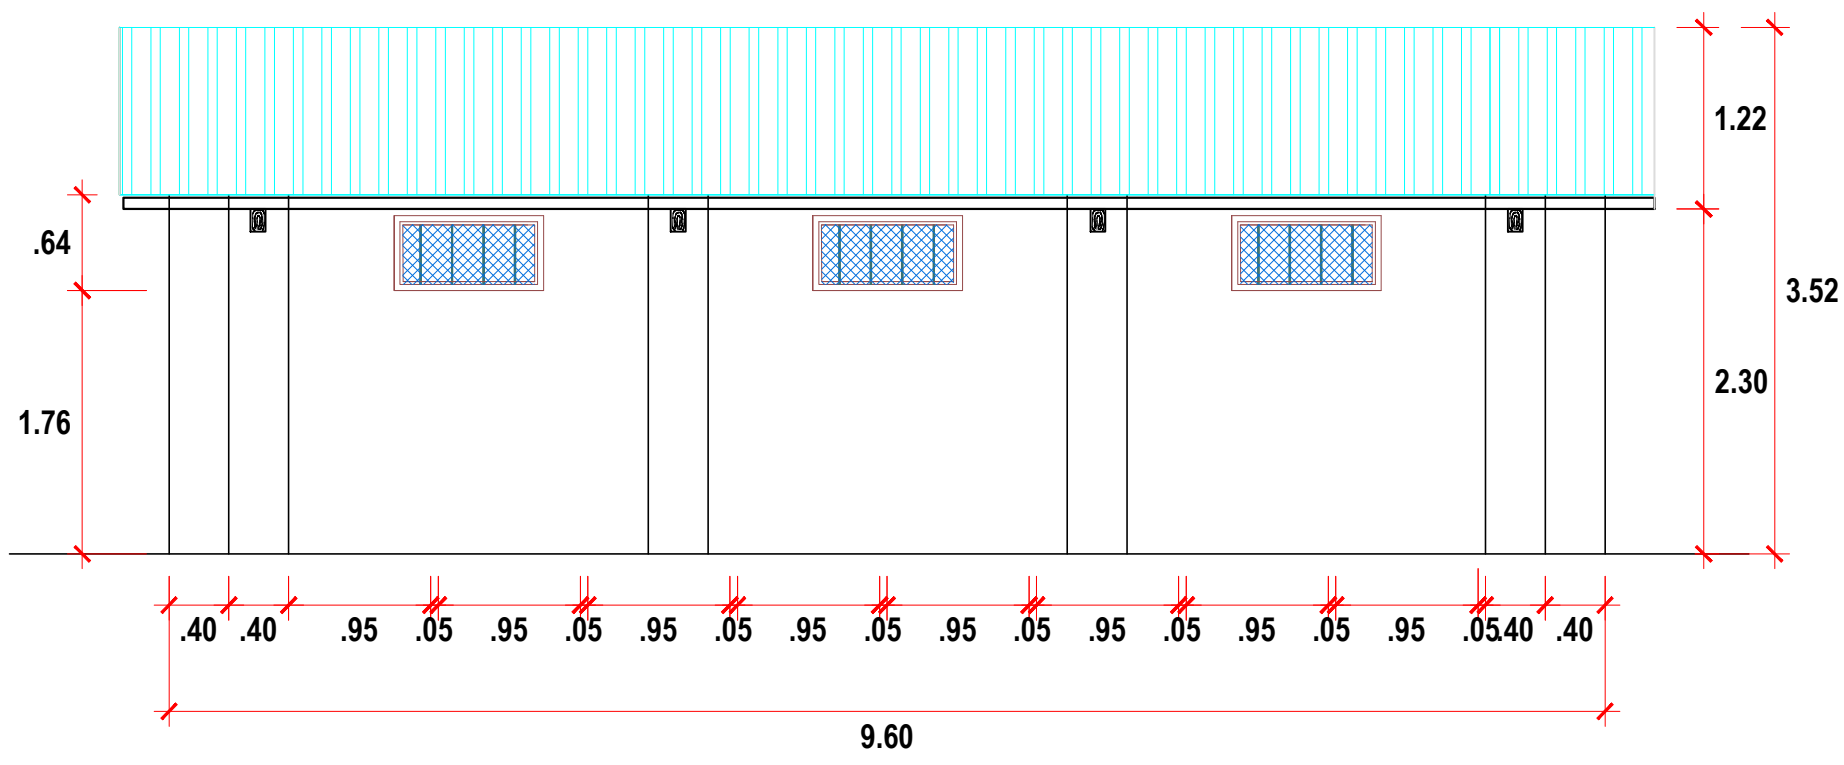

ELEVACION LATERAL

ESCALA : 1/50

"ASOCIACION DE PRODUCTORES AGROPECUARIOS LAMBRASHUAYCCO DE CASAORCCO (APAL)"					
PROYECTO: "MEJORAMIENTO EN LA PRODUCCION Y COMERCIALIZACION DE CUYES DE LA ASOCIACION DE PRODUCTORES AGROPECUARIOS LAMBRASHUAYCCO DE CASAORCCO (APAL) DEL DISTRITO DE CARMEN ALTO - PROVINCIA HUAMANGA - AYACUCHO"					LAMINA: A- 01
PLANO: ARQUITECTURA: DISTRIBUCION CORTE Y ELEVACION					
UBICACION:	DIBUJO:	DISEÑO:	PROYECTISTA:	APROBACION:	
Departamento: AYACUCHO	Dibujó: R.B.H	Diseño: Ing. R.B.H	Proyectista: Ing. R.B.H		
Provincia: HUAMANGA	Fecha:	Escala: INDICADA	VºBº:		
Ciudad: CARMEN ALTO					
País: CASAORCCO	AGOSTO 2020				