



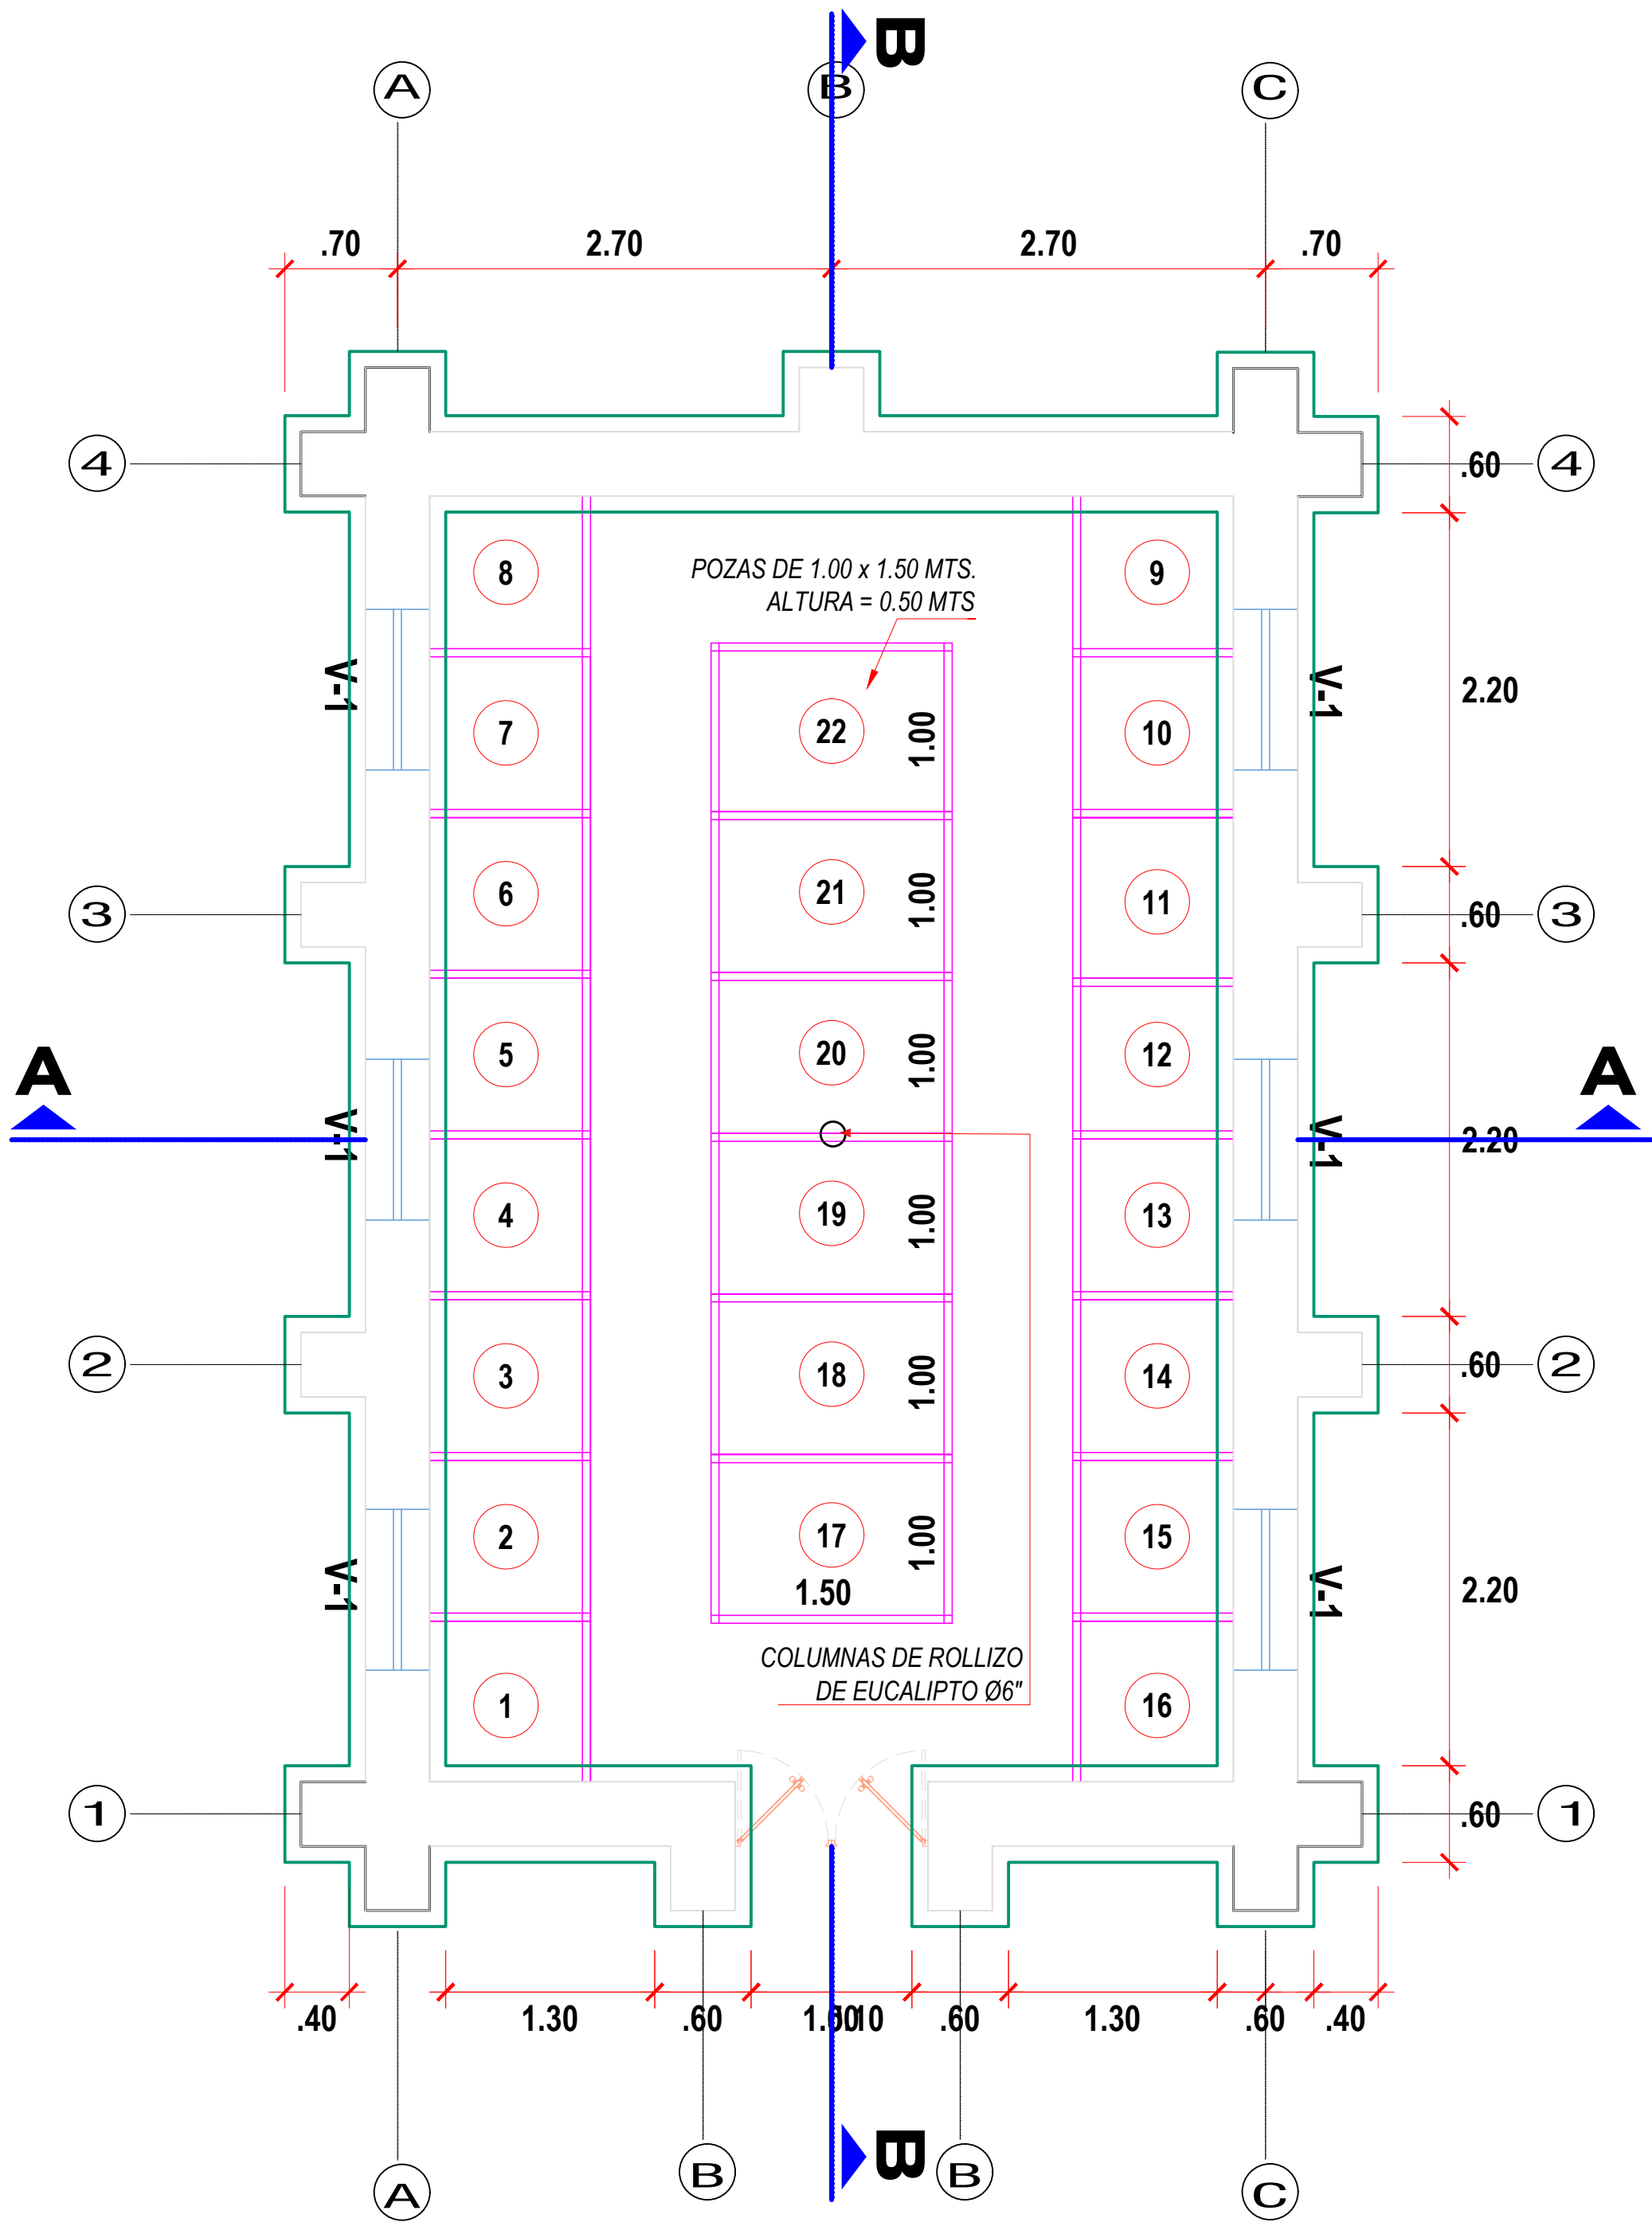


PLANO DE CIMENTACION

ESCALA : 1/50

ESPECIFICACIONES TECNICAS

CONCRETO :
CIMENTO MEZCLA BARRO + PM (6" máx)
SOBRECIMIENTO MEZCLA BARRO + PG (8" máx)
MUROS:
MURO DE ADOBE ASENTADO CON BARRO, 0.40*0.25*0.18

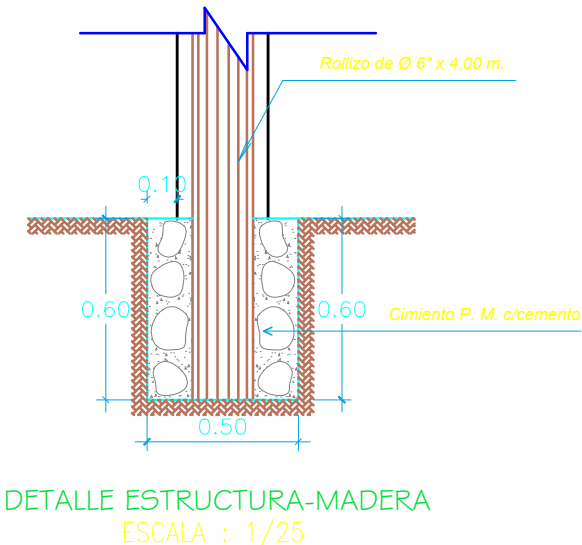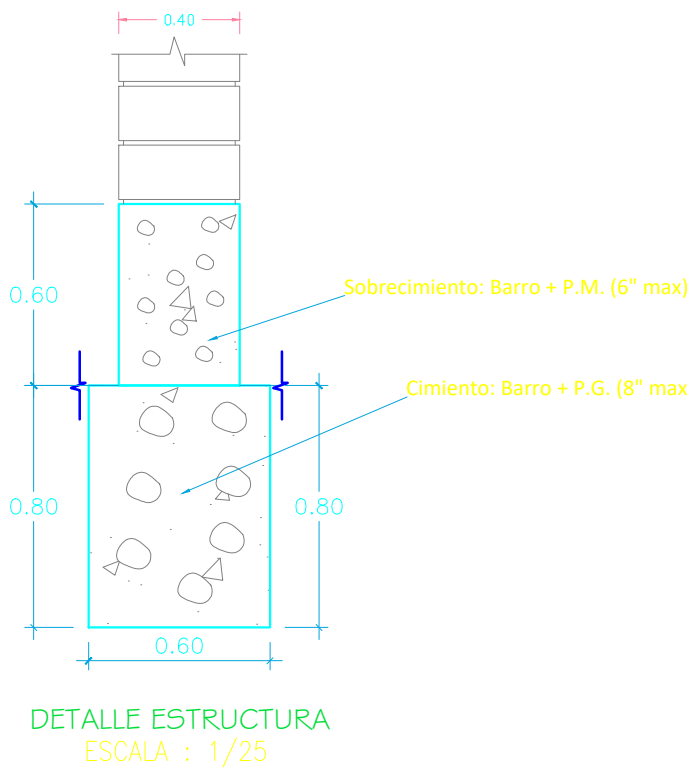

"ASOCIACION AGROPECUARIO DE PAMPARQUE "				
PROYECTO: "MEJORAMIENTO EN LA PRODUCCION Y COMERCIALIZACION DE CUYES EN LA ASOCIACION AGROPECUARIO DE PAMPARQUE DEL DISTRITO DE PUQUIO, PROVINCIA LUCANAS-AYACUCHO".			LAMINA: E- 01	
PLANO: PLANO DE CIMENTACION				
UBICACION : Departamento : AYACUCHO Provincia : LUCANAS Distrito : PUQUIO Sector: PAMPARQUE		DIBUJO: R.B.H	DISEÑO: Ing. K.B.H	PROYECTISTA: Ing. K.B.H
		FECHA: AGOSTO 2020	ESCALA: INDICADA	V"B":
		APROBACION:		