



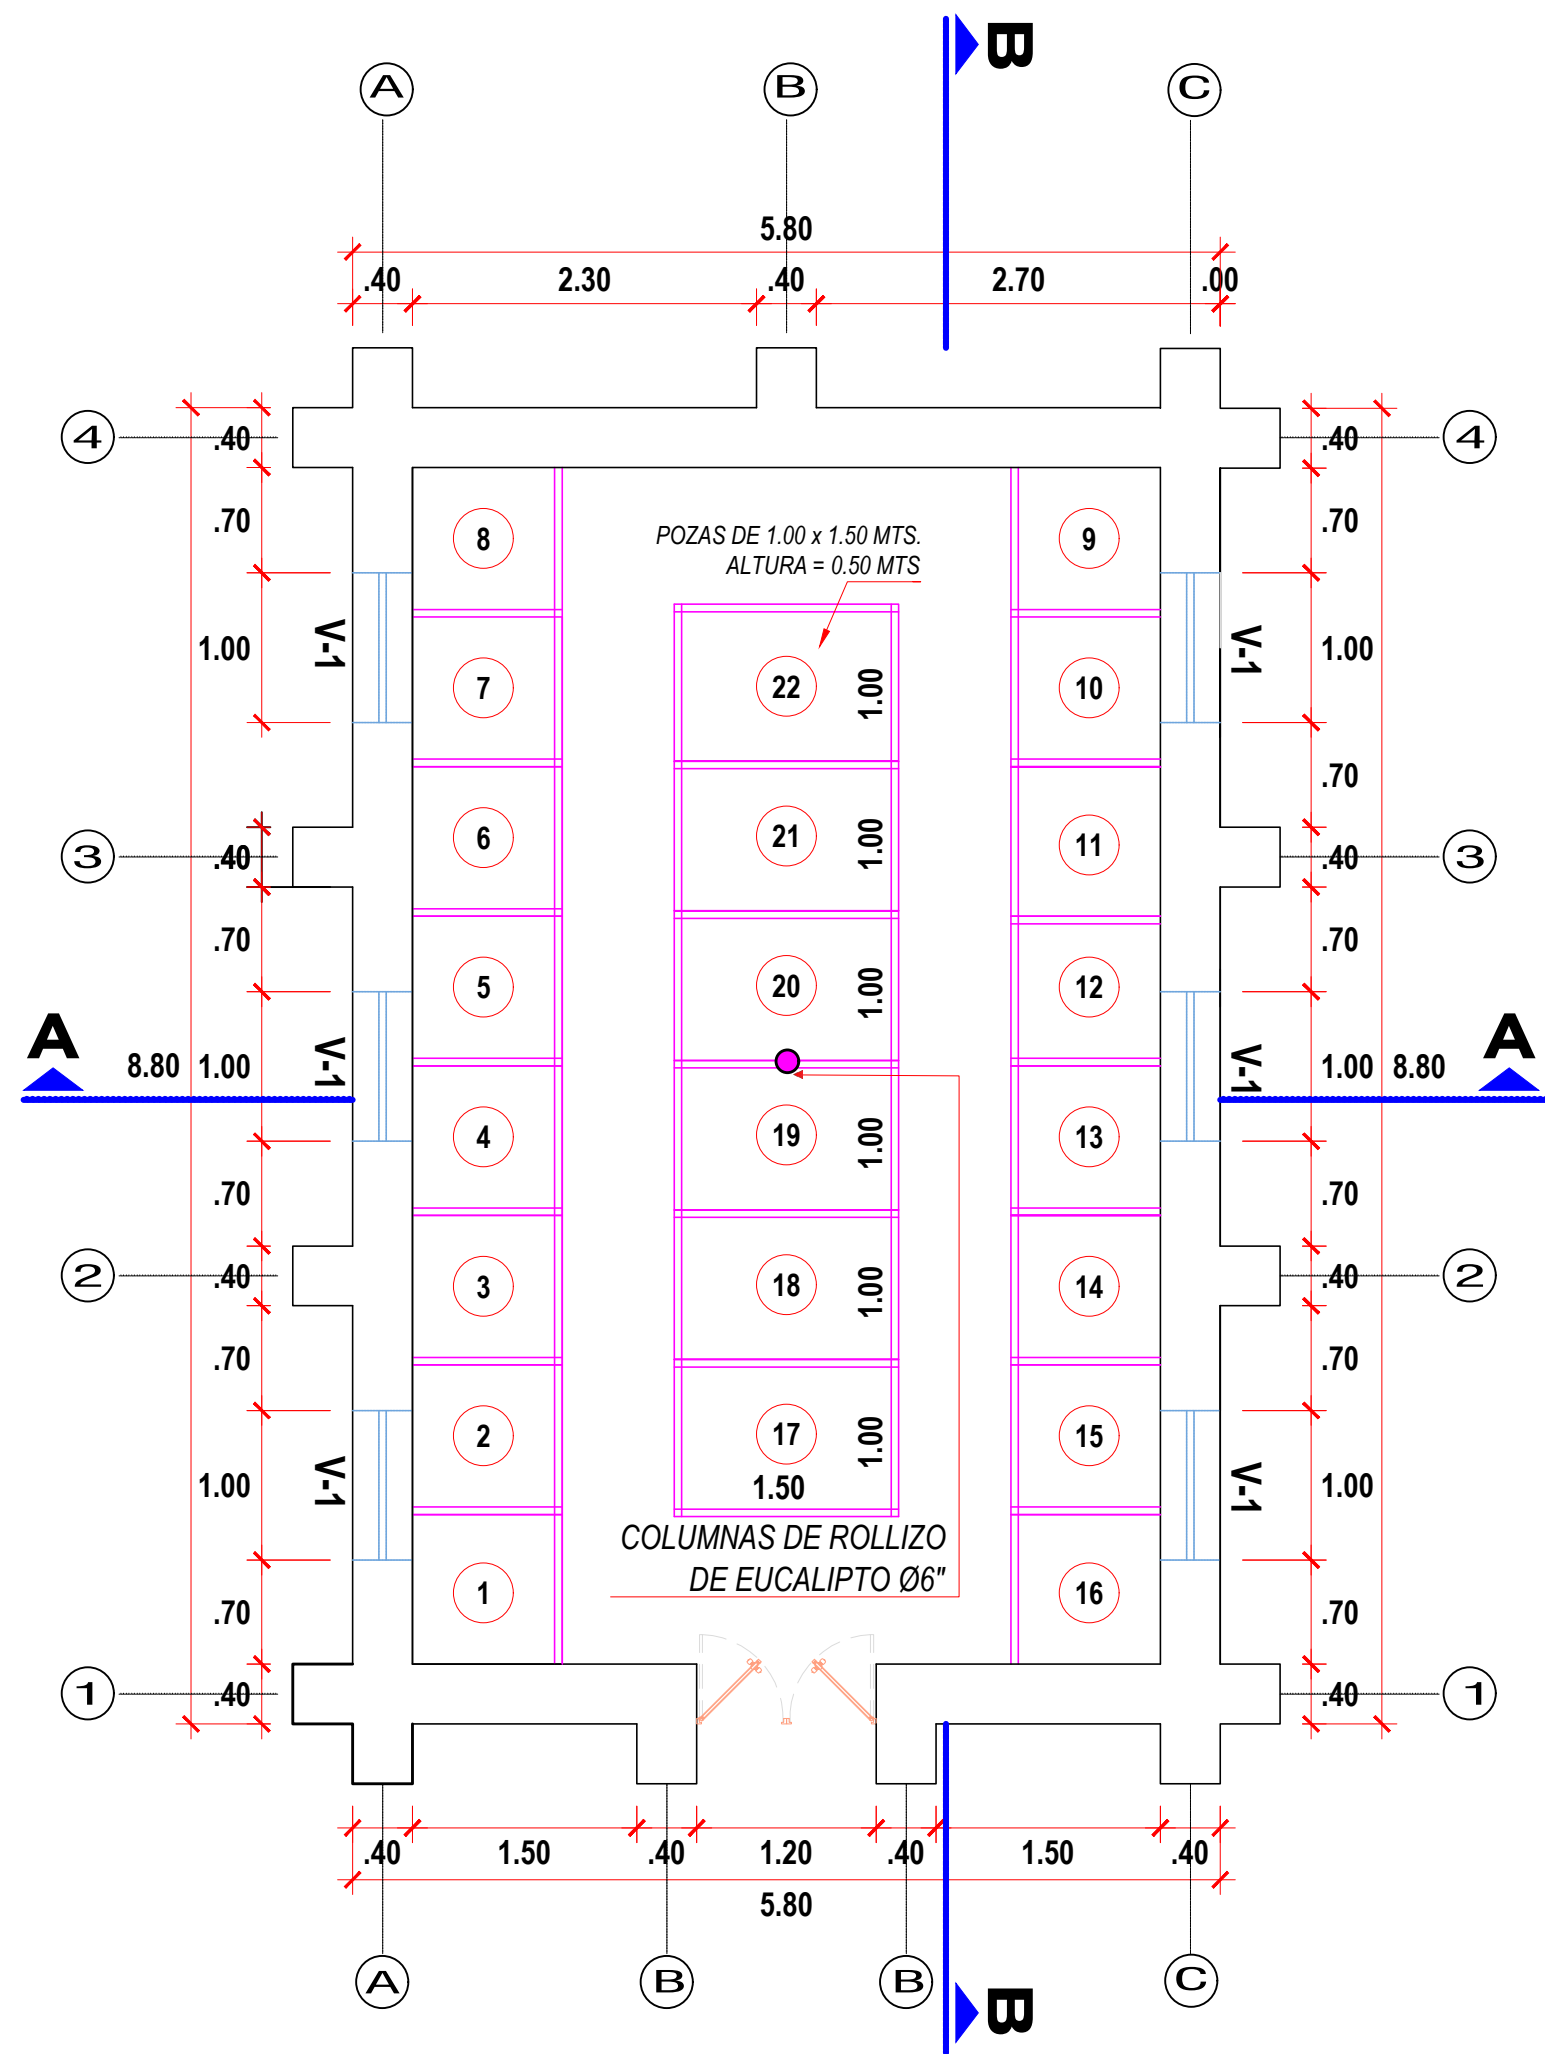


DISTRIBUCION


ESCALA : 1/50

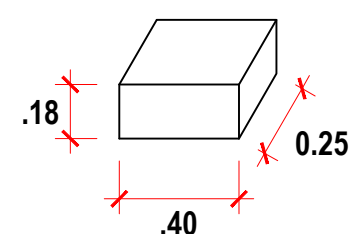


ADOBE TIPICO

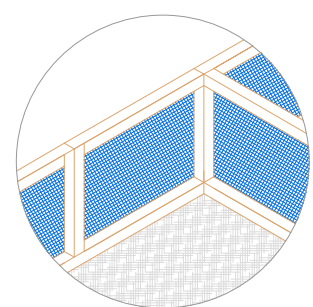

ISOMETRICO DE POSA DE CUY DE MALLA METALICO CON MARCO DE MADERA

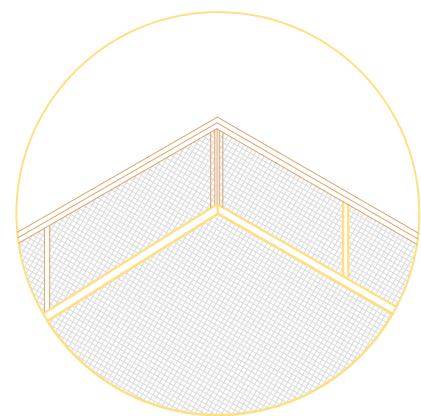


UNIONES PERSPECTIVA

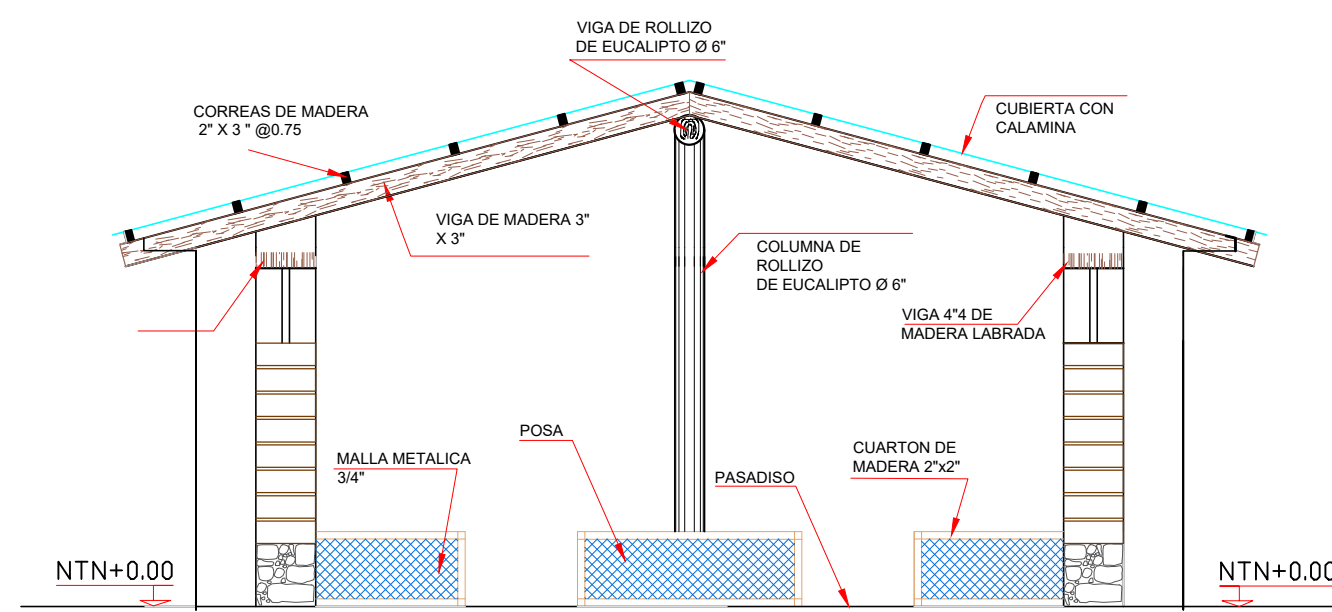

CORTE A-A


ESCALA : 1/50

CUADRO DE VANDOS						
TIPO	ANCHO	ALTO	ALFEIZAR	ESTRUCTURA	NOMBRE	CANT.
V1	1.00	0.50	1.76	MARCO DE MADERA CON MALLA MOSQUETERO	VENTANA TIPO V1	6
P1	1.20	2.00	-	MARCO DE MADERA DE 2 HOJAS CON CALAMINA	PUERTA TIPO P1	1

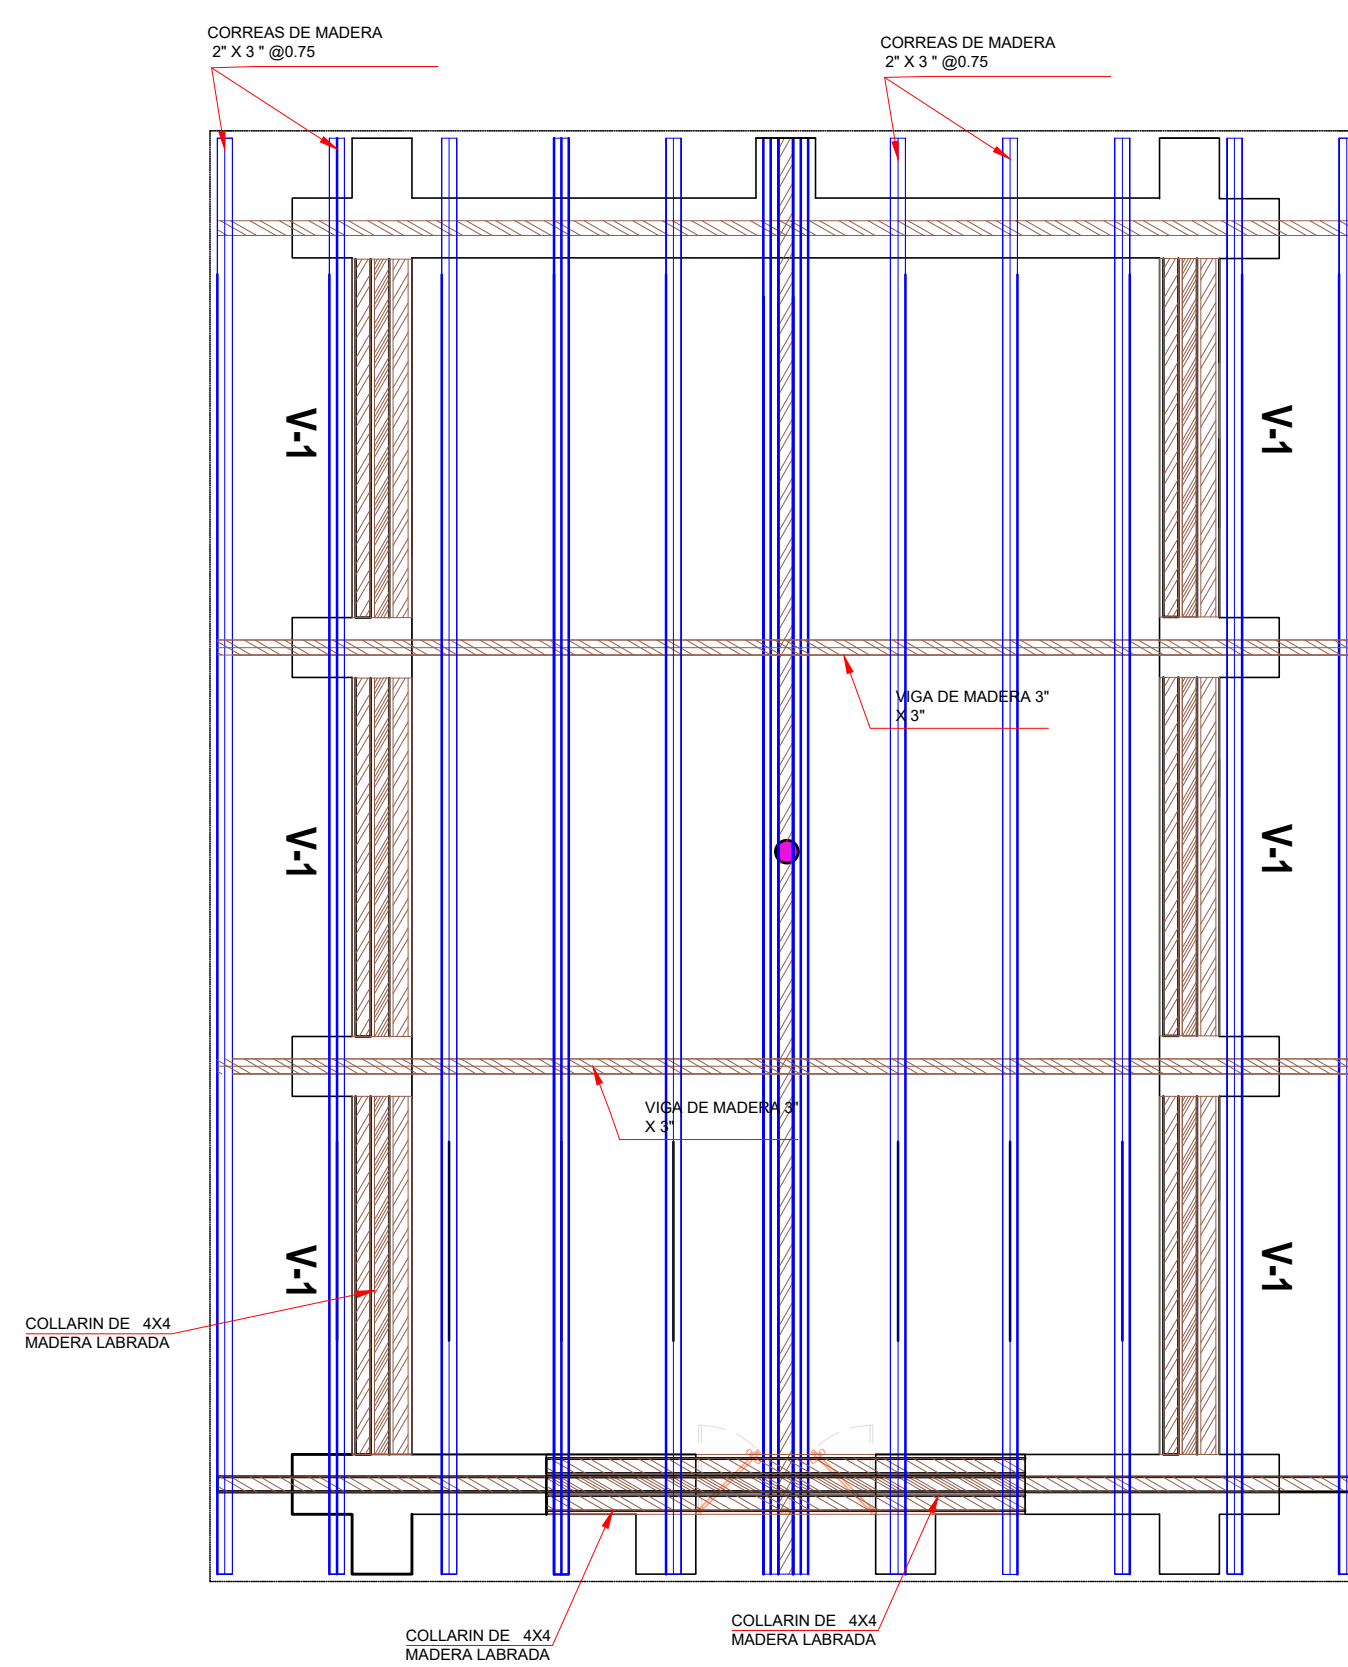


ESTRUCTURA DE TECHO

ESCALA : 1/50

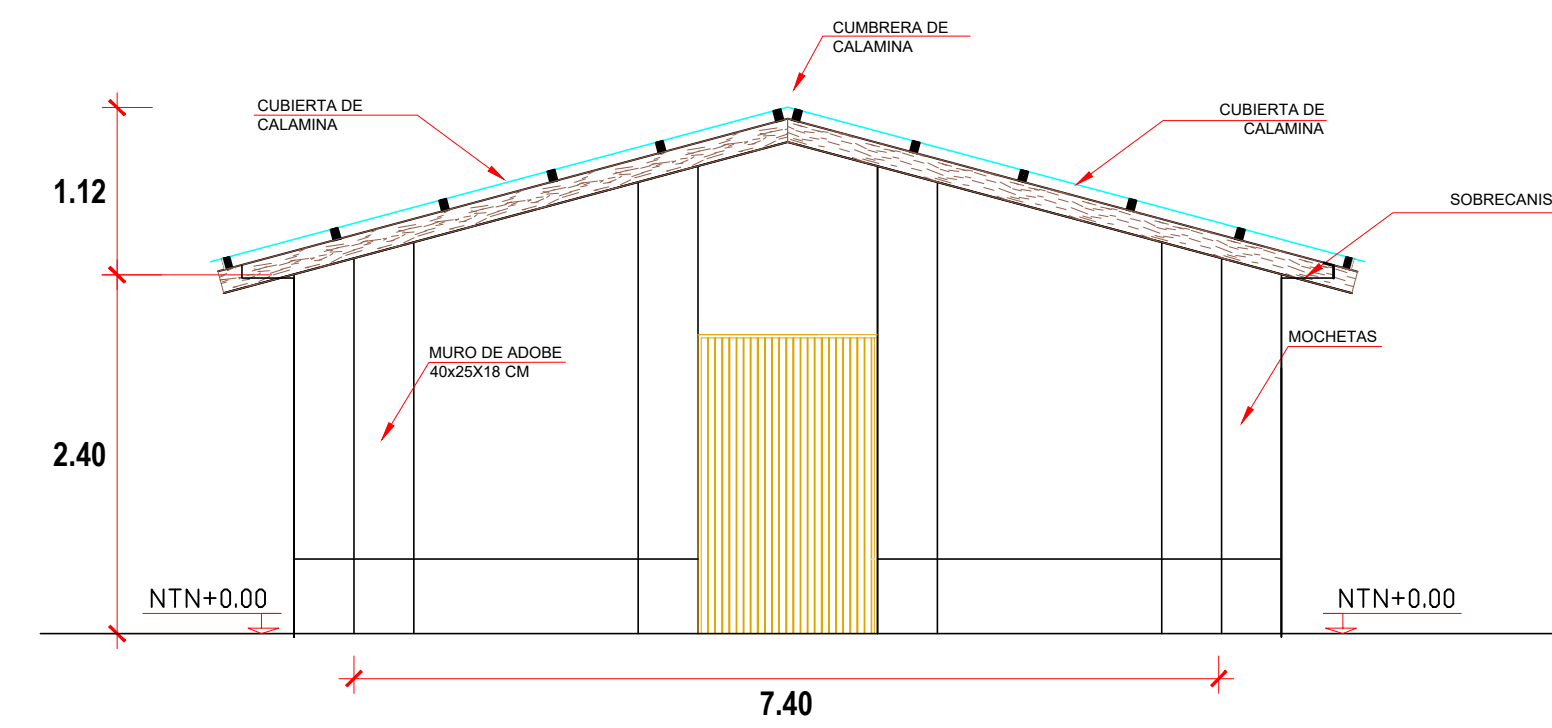


ELEVACION FRONTAL

ESCALA : 1/50

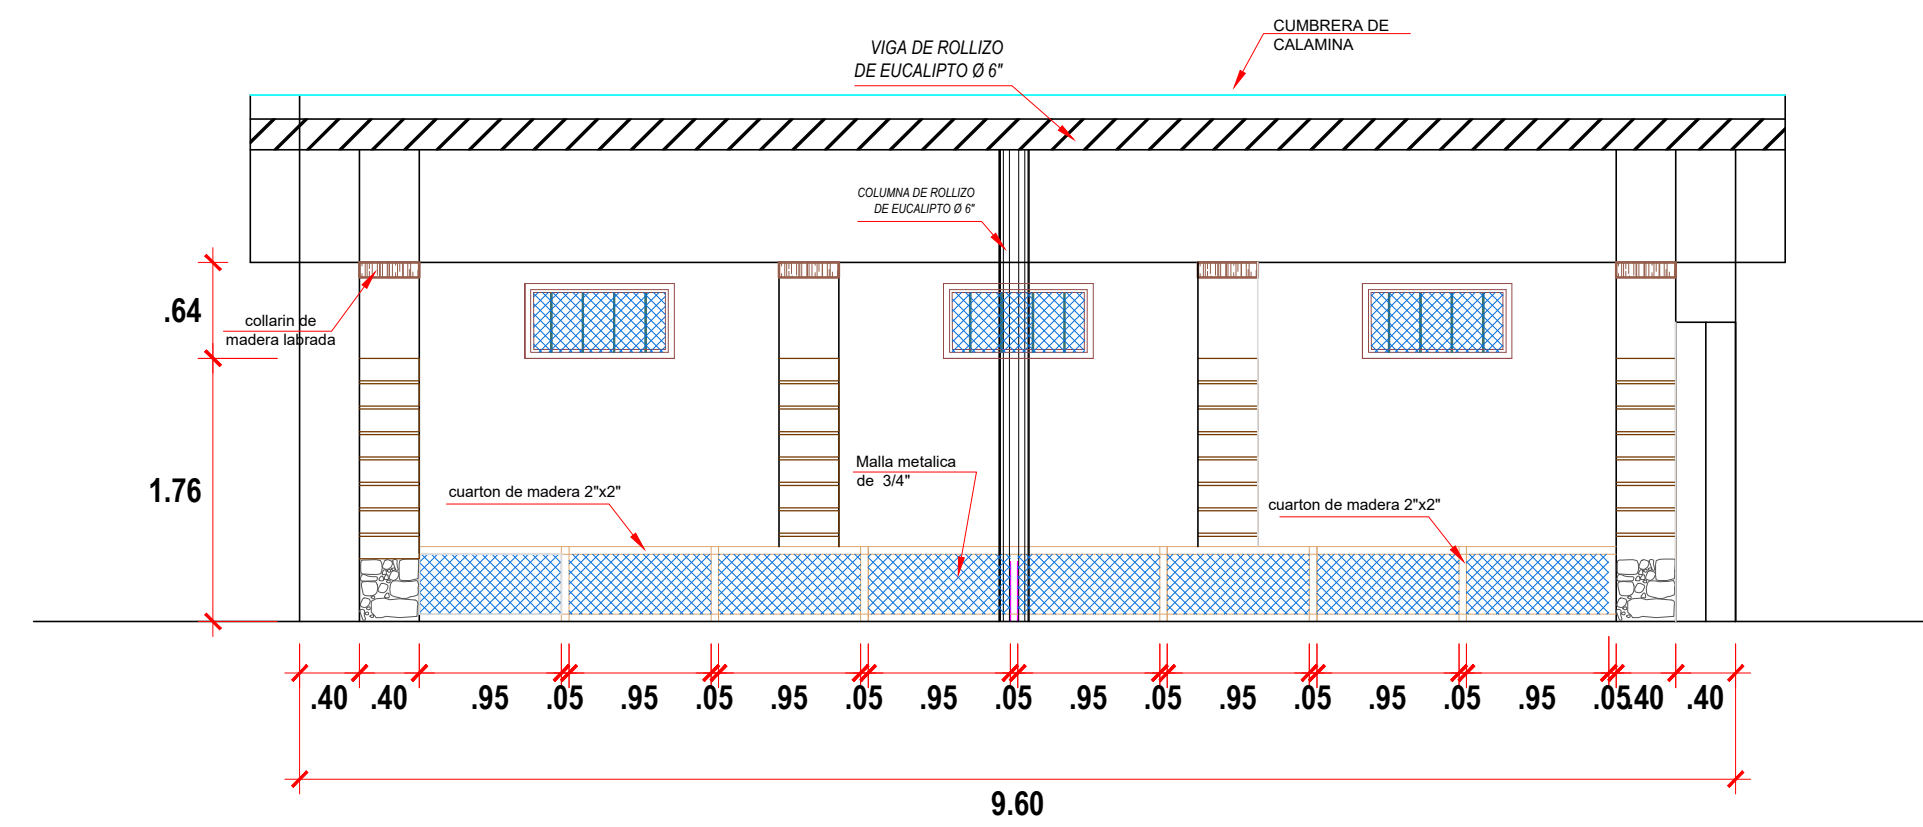

CORTE B-B

ESCALA : 1/50

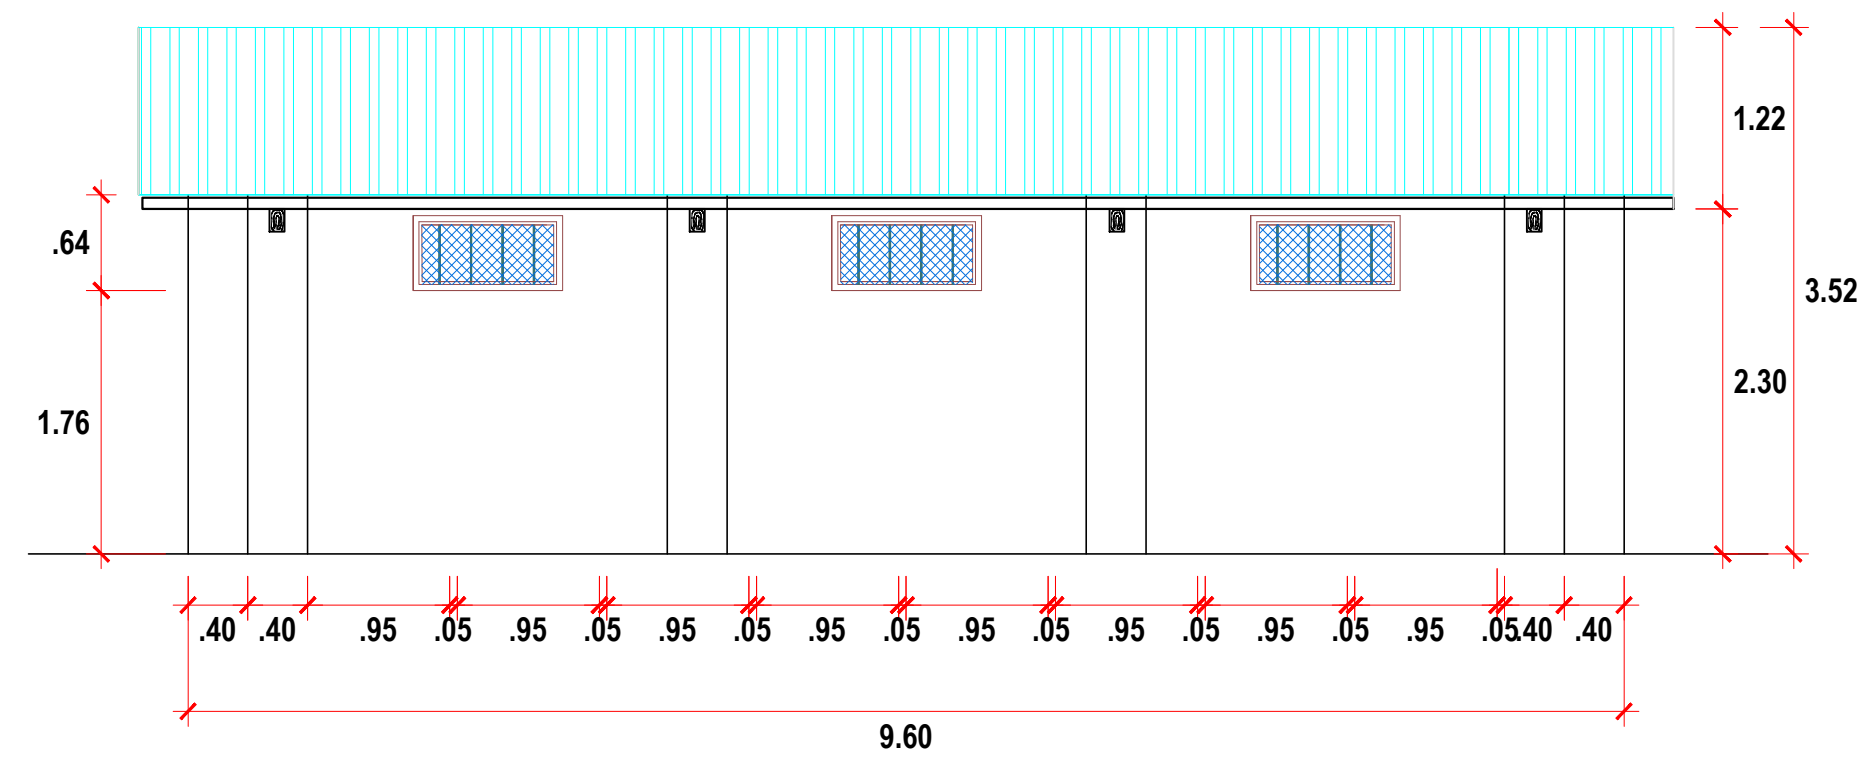

ELEVACION LATERAL

ESCALA : 1/50

"ASOCIACION AGROPECUARIO DE PAMPARQUE "					
PROYECTO: "MEJORAMIENTO EN LA PRODUCCION Y COMERCIALIZACION DE CUYES EN LA ASOCIACION AGROPECUARIO DE PAMPARQUE DEL DISTRITO DE PUQUIO, PROVINCIA LUCANAS-AYACUCHO"				LAMINA:	
PLANO: ARQUITECTURA: DISTRIBUCION CORTE Y ELEVACION				A-01	
UBICACION :	DIBUJO:	DISEÑO:	PROYECTISTA:	APROBACION:	
Departamento: AYACUCHO	Dibujante: R.B.H	Diseñador: Ing. R.B.H	Proyectista: Ing. R.B.H		
Provincia: LUCANAS	FECHA:	ESCALA:	VºBº:		
Ciudad: PUQUIO	AGOSTO 2020	INDICADA			
Sector: PAMPARQUE					